



REVISIONS	
NUM.	DATE


SHEET CONTENTS
REBAR
DETAILS

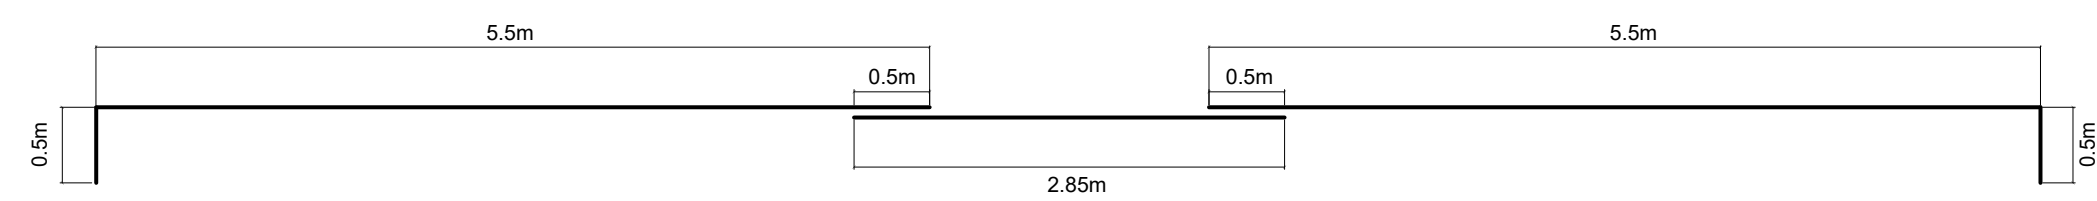


3 Section
Rebar Overlap Detail, Typ. 1:50

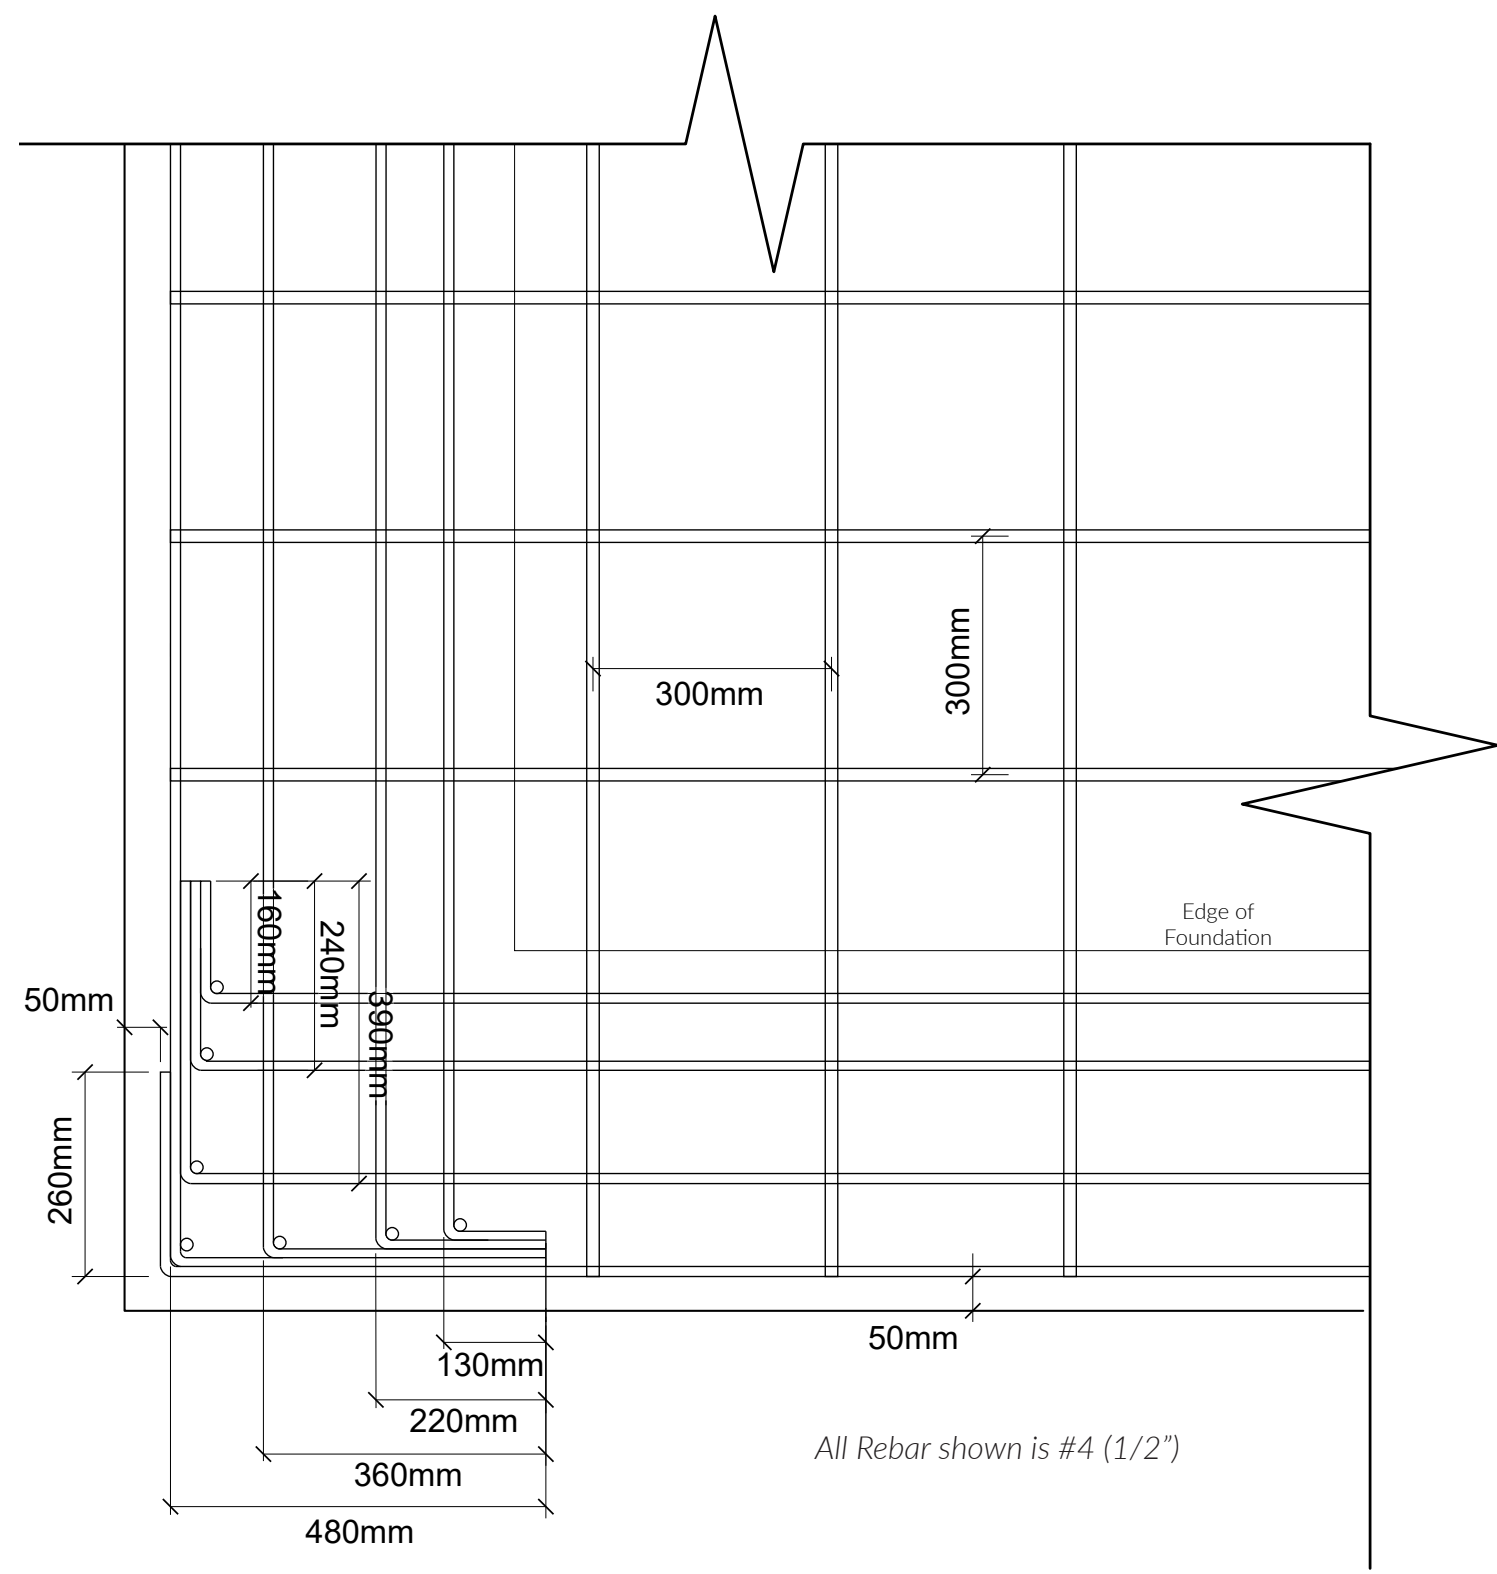

2 Plan
Slab Corner Detail 1:10

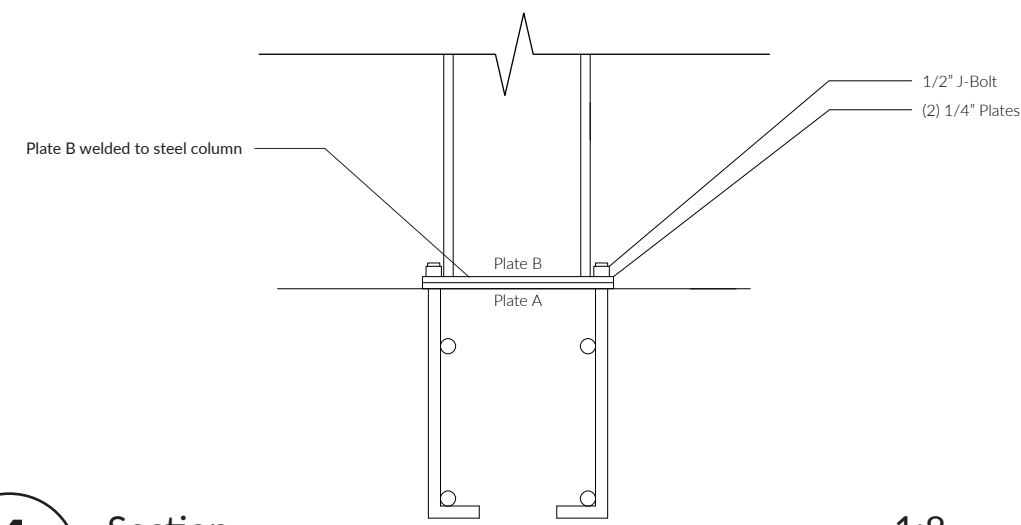

4 Section
Column @ Plate 1:8

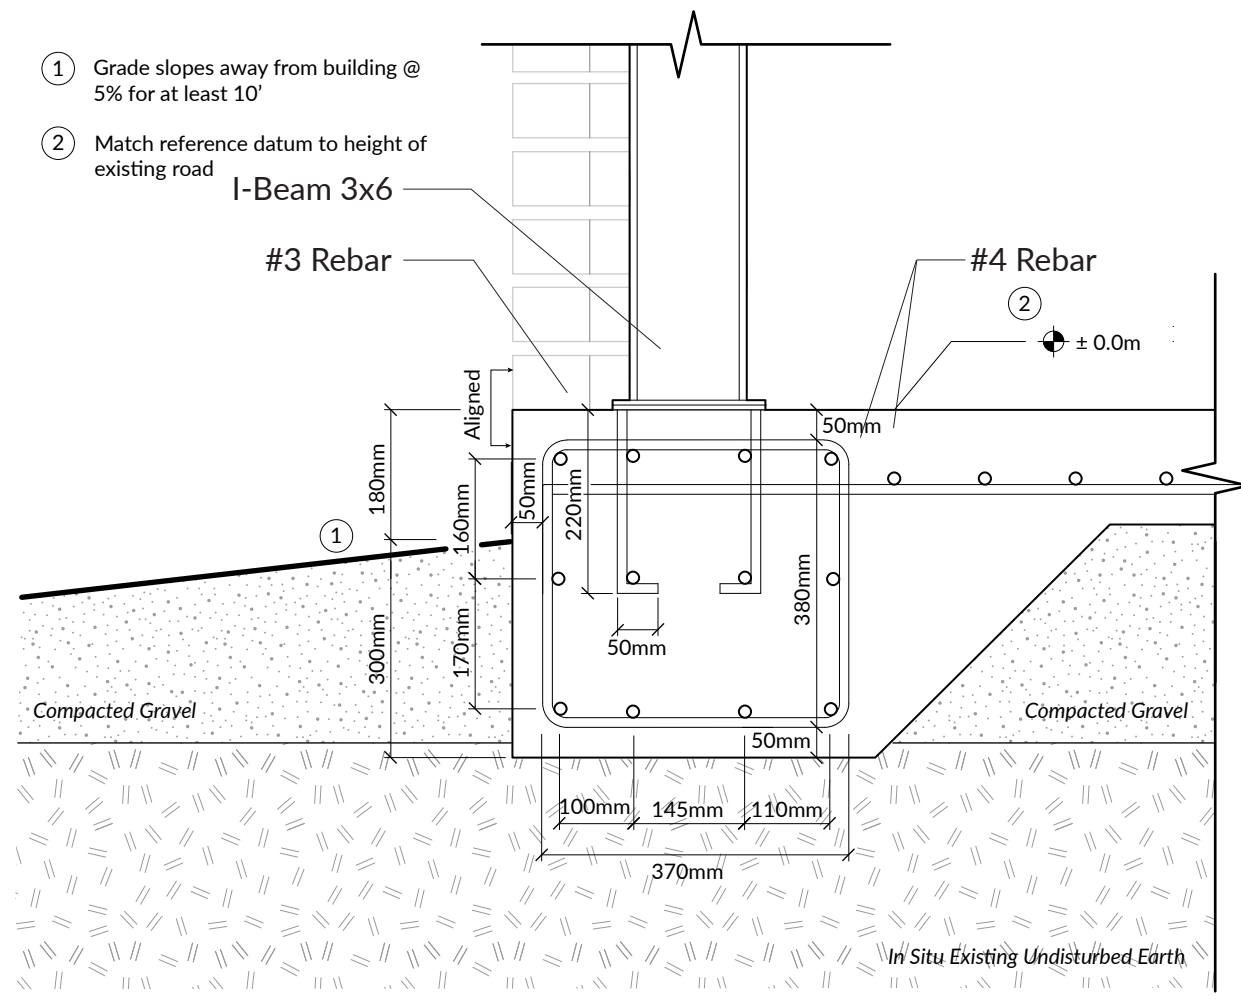

1 Section
Column @ Foundation 1:10