



Pipe holes to move according to rebar schedule

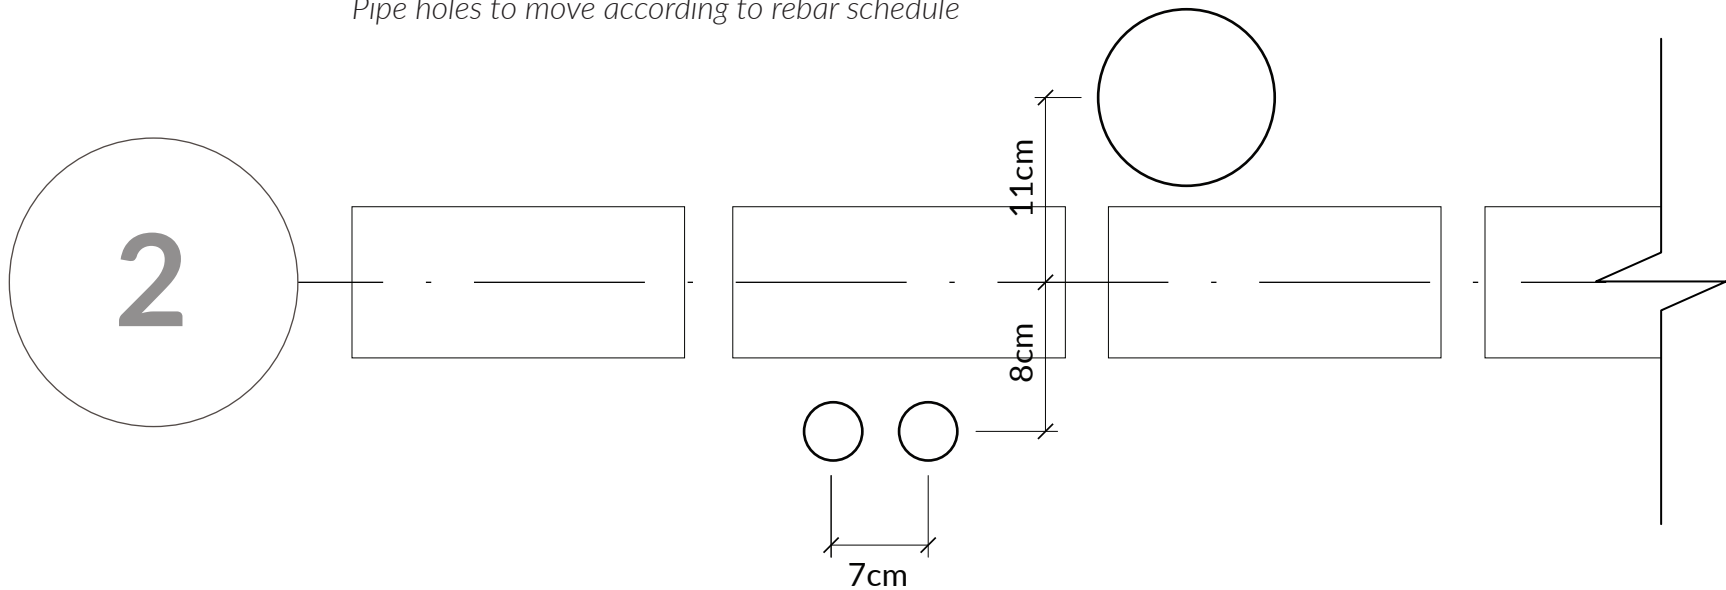

2 Plan 1:5
Plumbing Hole Detail

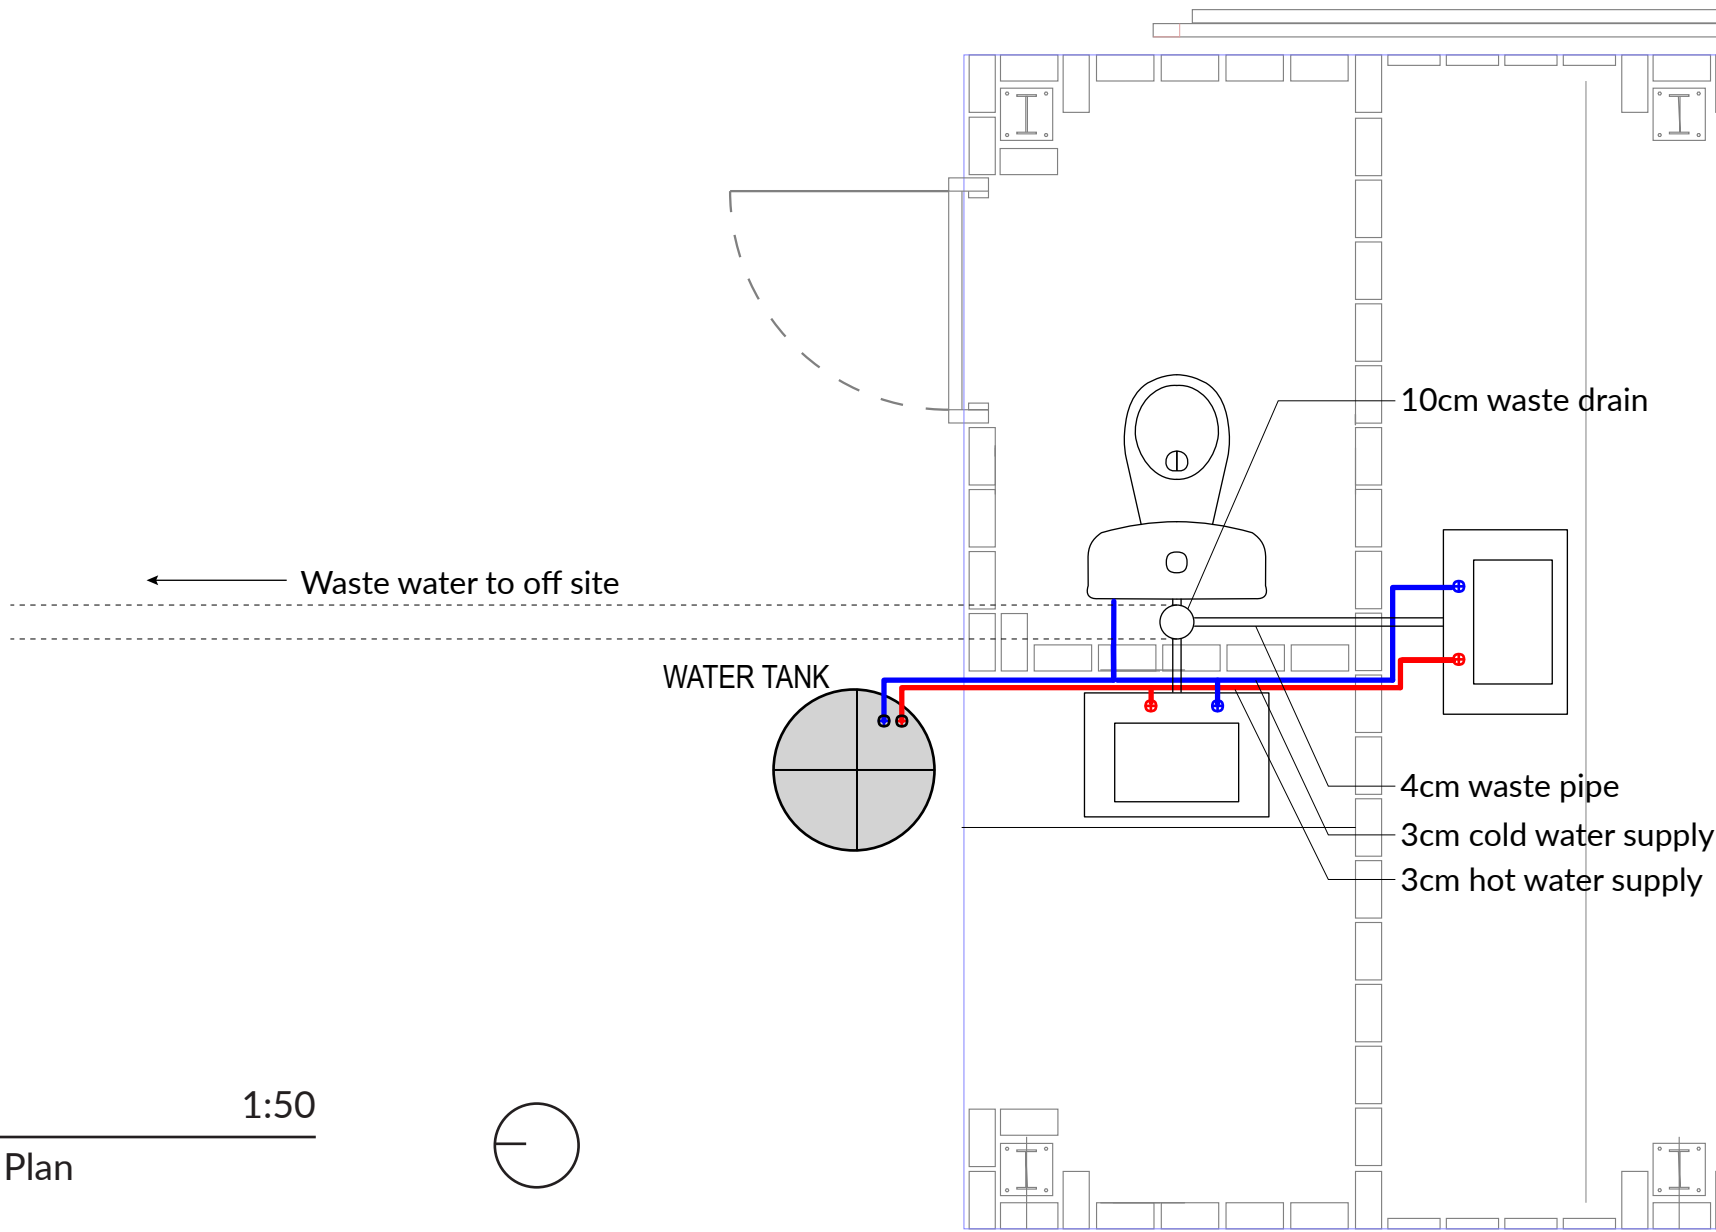

1 Plan 1:50
Plumbing Plan

REVISIONS	
NUM.	DATE

SHEET CONTENTS
PLUMBING
PLAN