



REVISIONS	
NUM.	DATE

SHEET CONTENTS
DOOR
DETAILS

A8.1

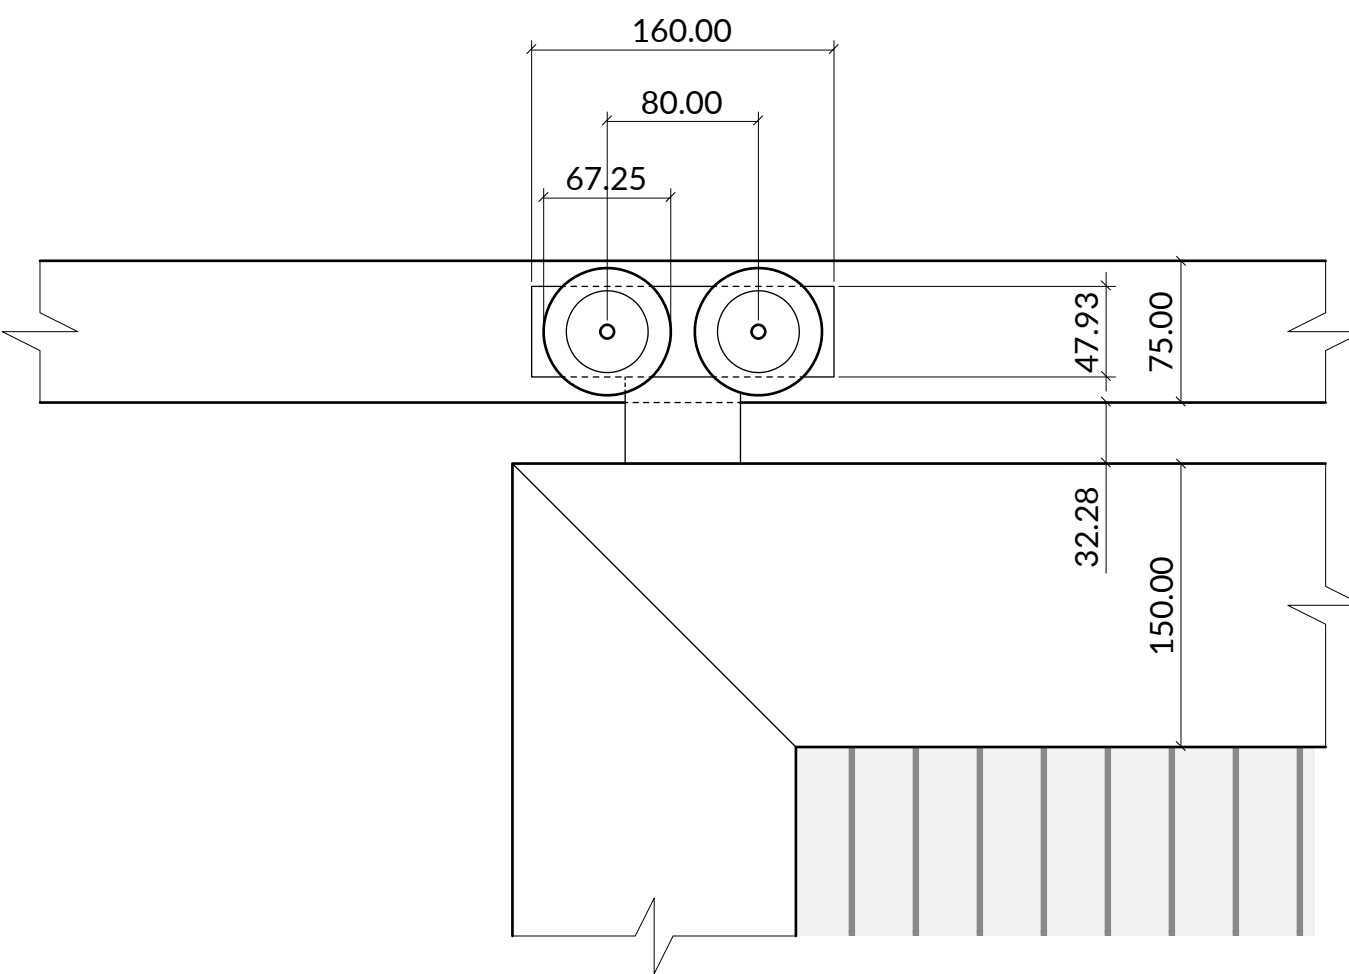

2 Elevation 1:4
Door Corner Detail

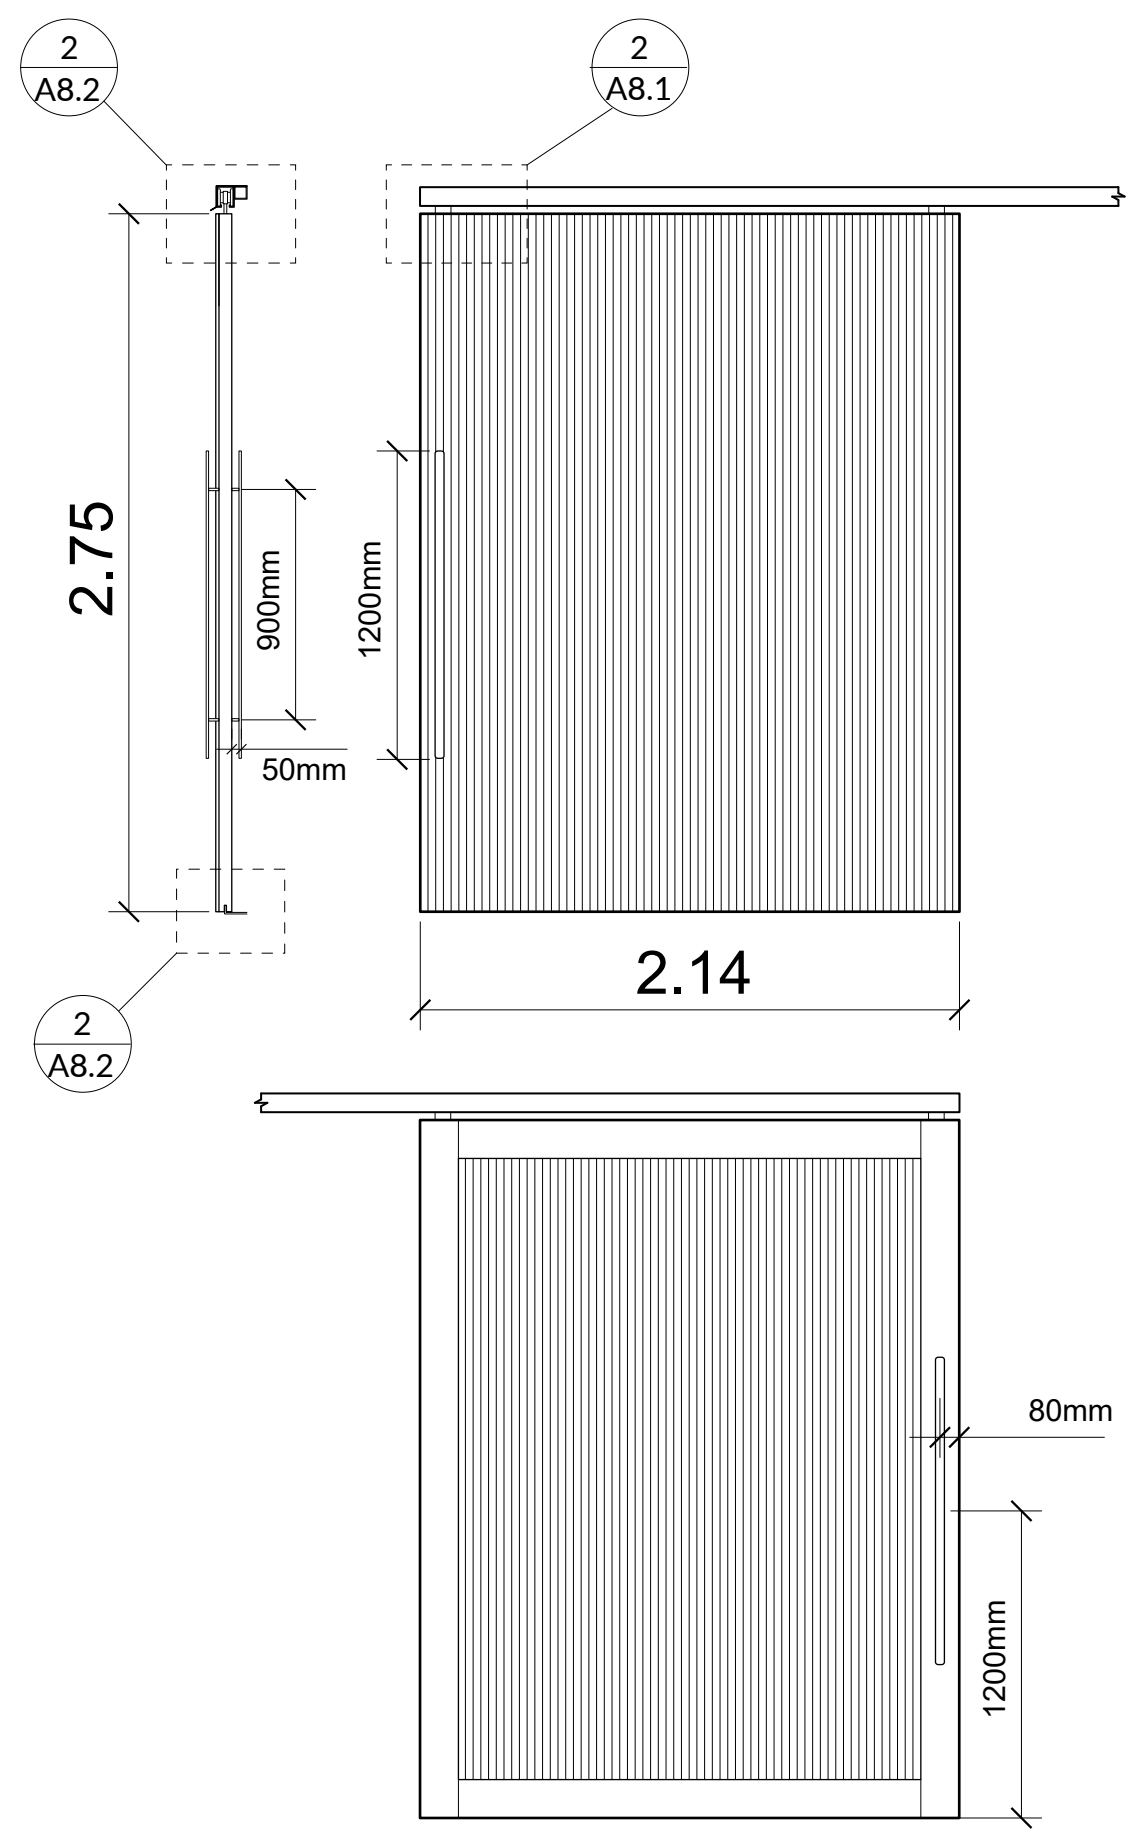

1 Elevation 1:30
Barn Door, Typ.